


मोहा , ता. जी. यवतमाळ , येथील गट नं /सर्वे नं. २५२ मधील ले आऊटचे मोजणी रेखाचीत्र  
गो. र. कं . -- १० / तातडी / बीगरशेती / २०२४  
राजदार -- श्री चिंधु चिंतामण देवकर.  
मोजणी दि. -- २६/०३/२०२४

३०

मोजणीस हृजर ईसम

मोजणीस हृजर ईसम

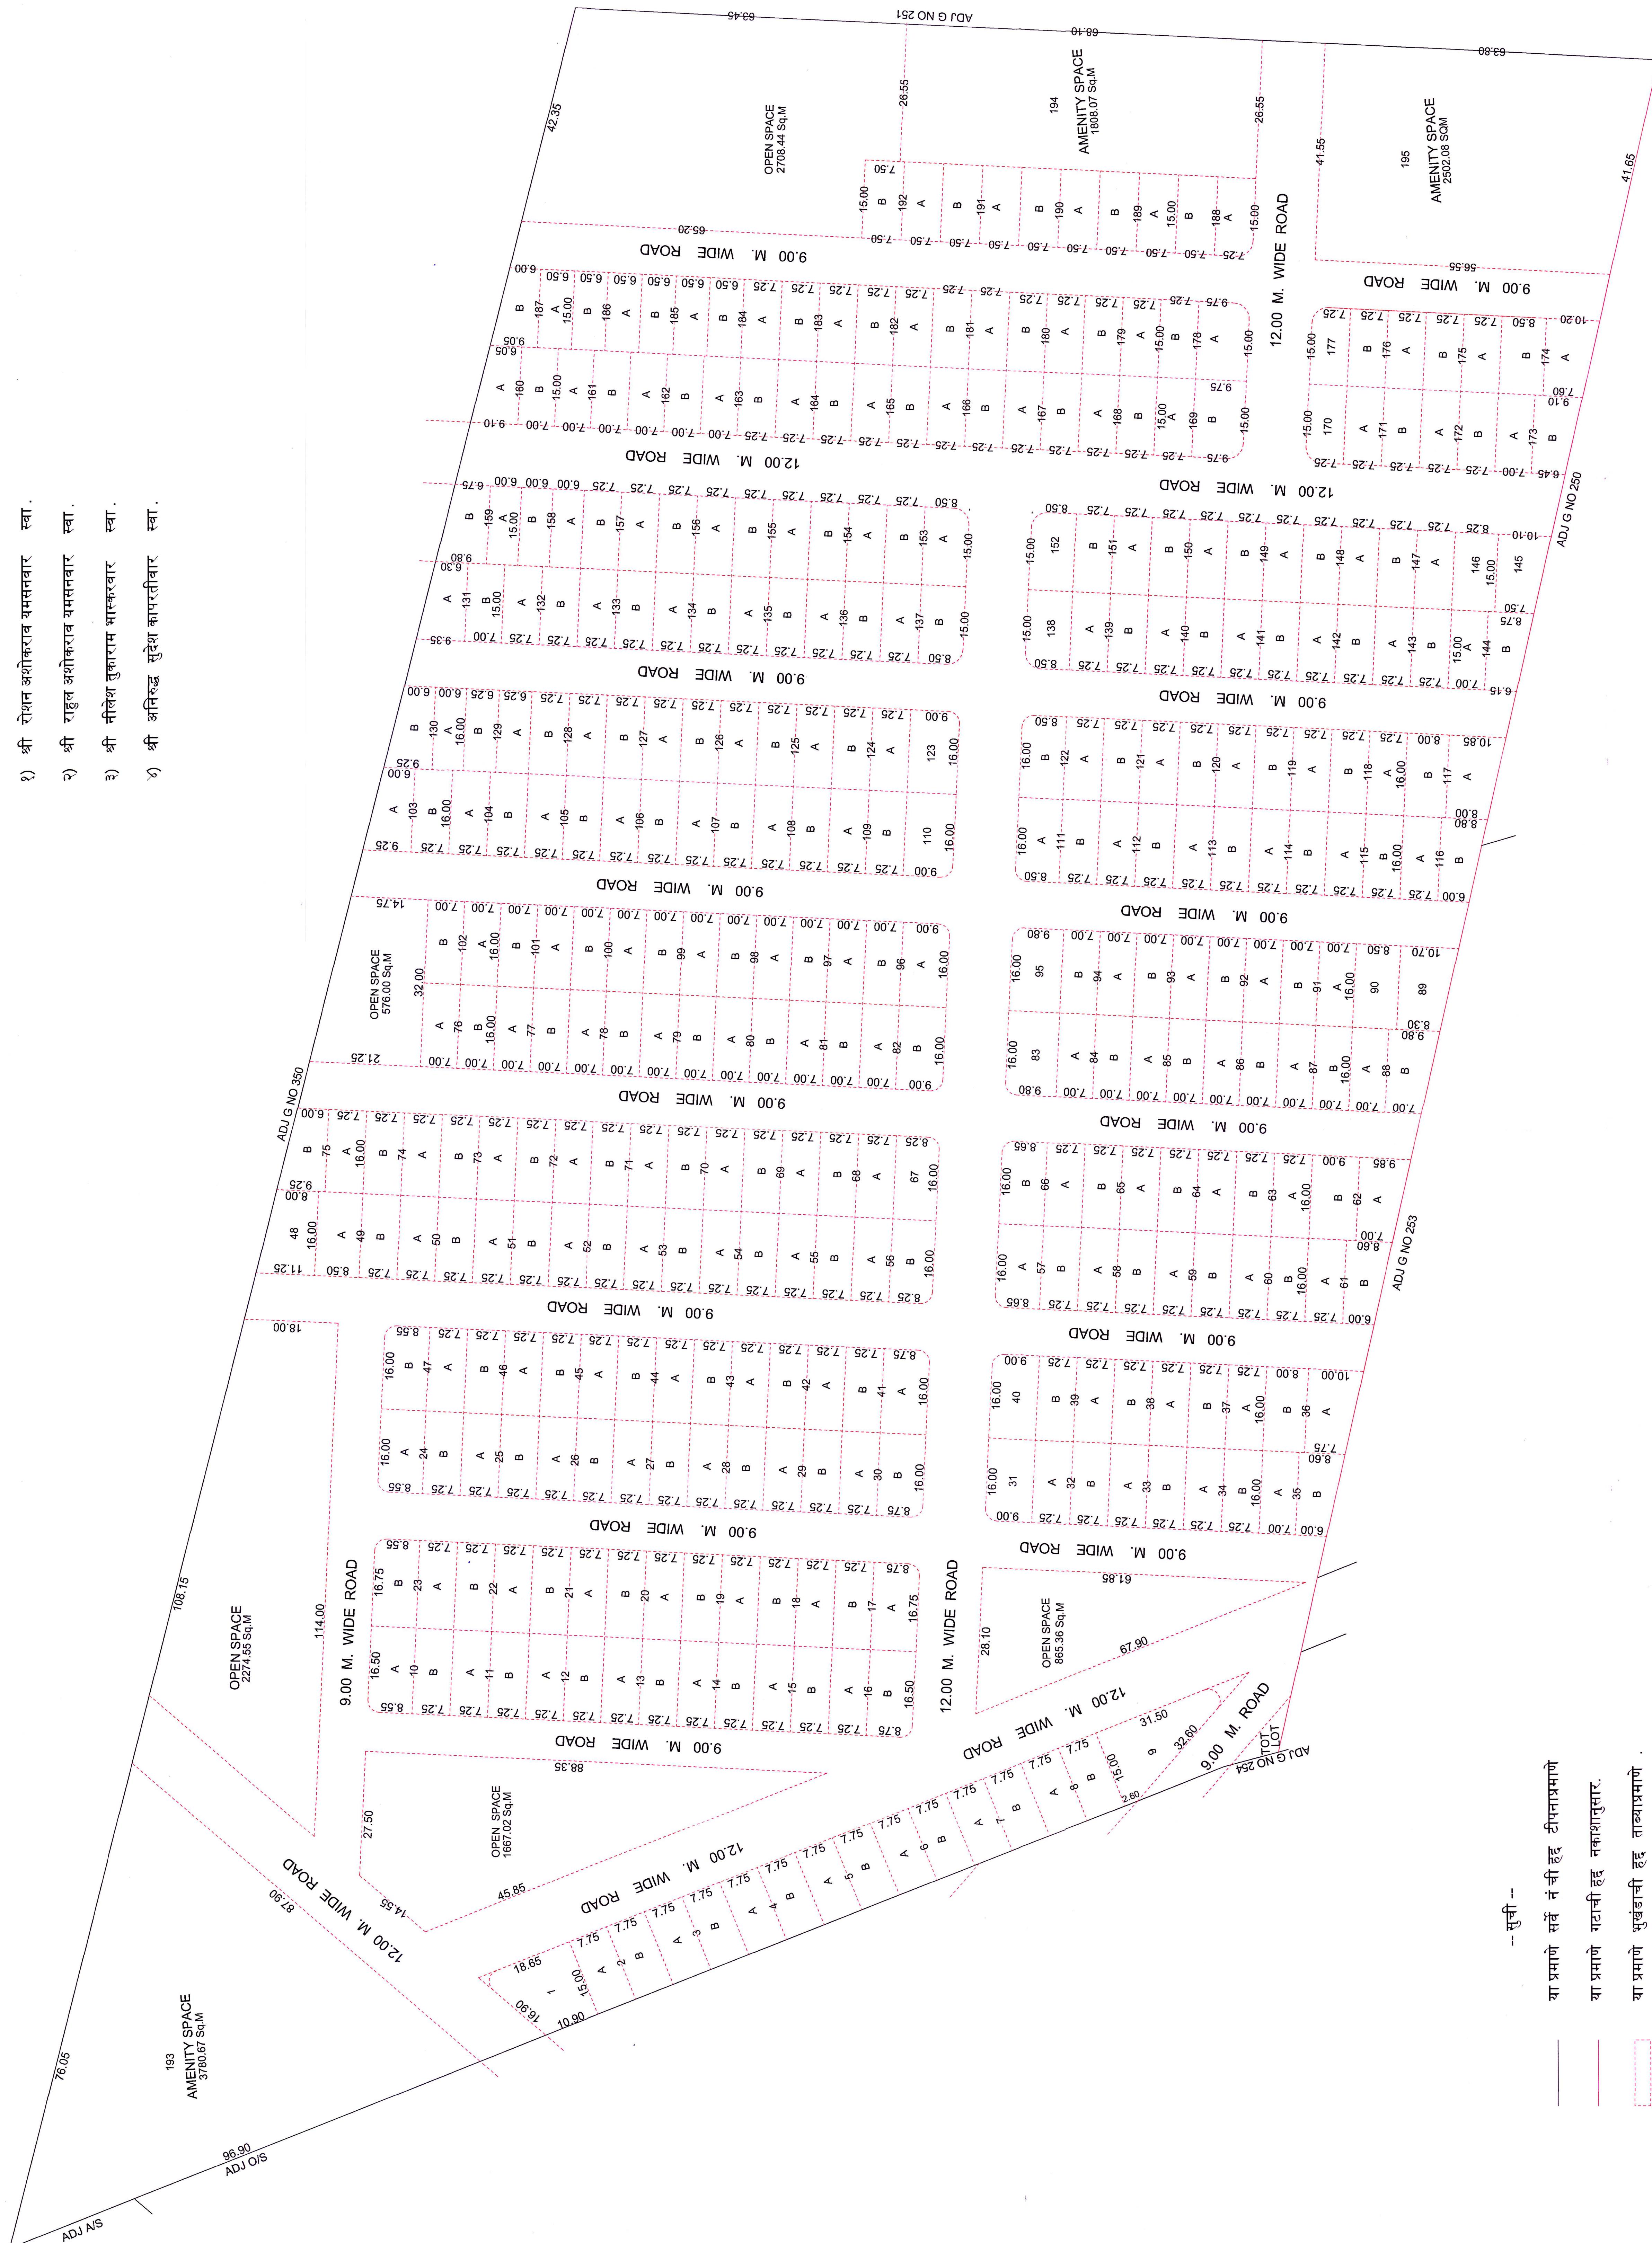

AREA STATEMENT	
TOTAL AREA OF LAND AS PER 7/12 ( GAT. NO.252 = 8.09 HE.)	80900.00 Sq.M
AREA UNDER RESI PLOT	42513.37 Sq.M
AREA UNDER OPEN SPACE	8091.37 Sq.M
AREA UNDER AMENITY SPACE PL NO 274 ( PL. NO.193 = 3780.67 Sq.M + PL NO 194 = 1808.07 Sq M) + PL. NO.195 = 2502.08 Sq.M)	8090.82 Sq.M
AREA UNDER ROAD & CURVE	22204.44 Sq.M

प्रमाण १ : ५

मोजणी करण

विजय सुरोः भूकमापक

कौतूहलीकौतूहलीकौतूहलीकौतूहली

उप अधिकारक घूसी अधिलेख व्यवस्थापन दाता

२०२३ मध्ये अगस्त महिन्यात

